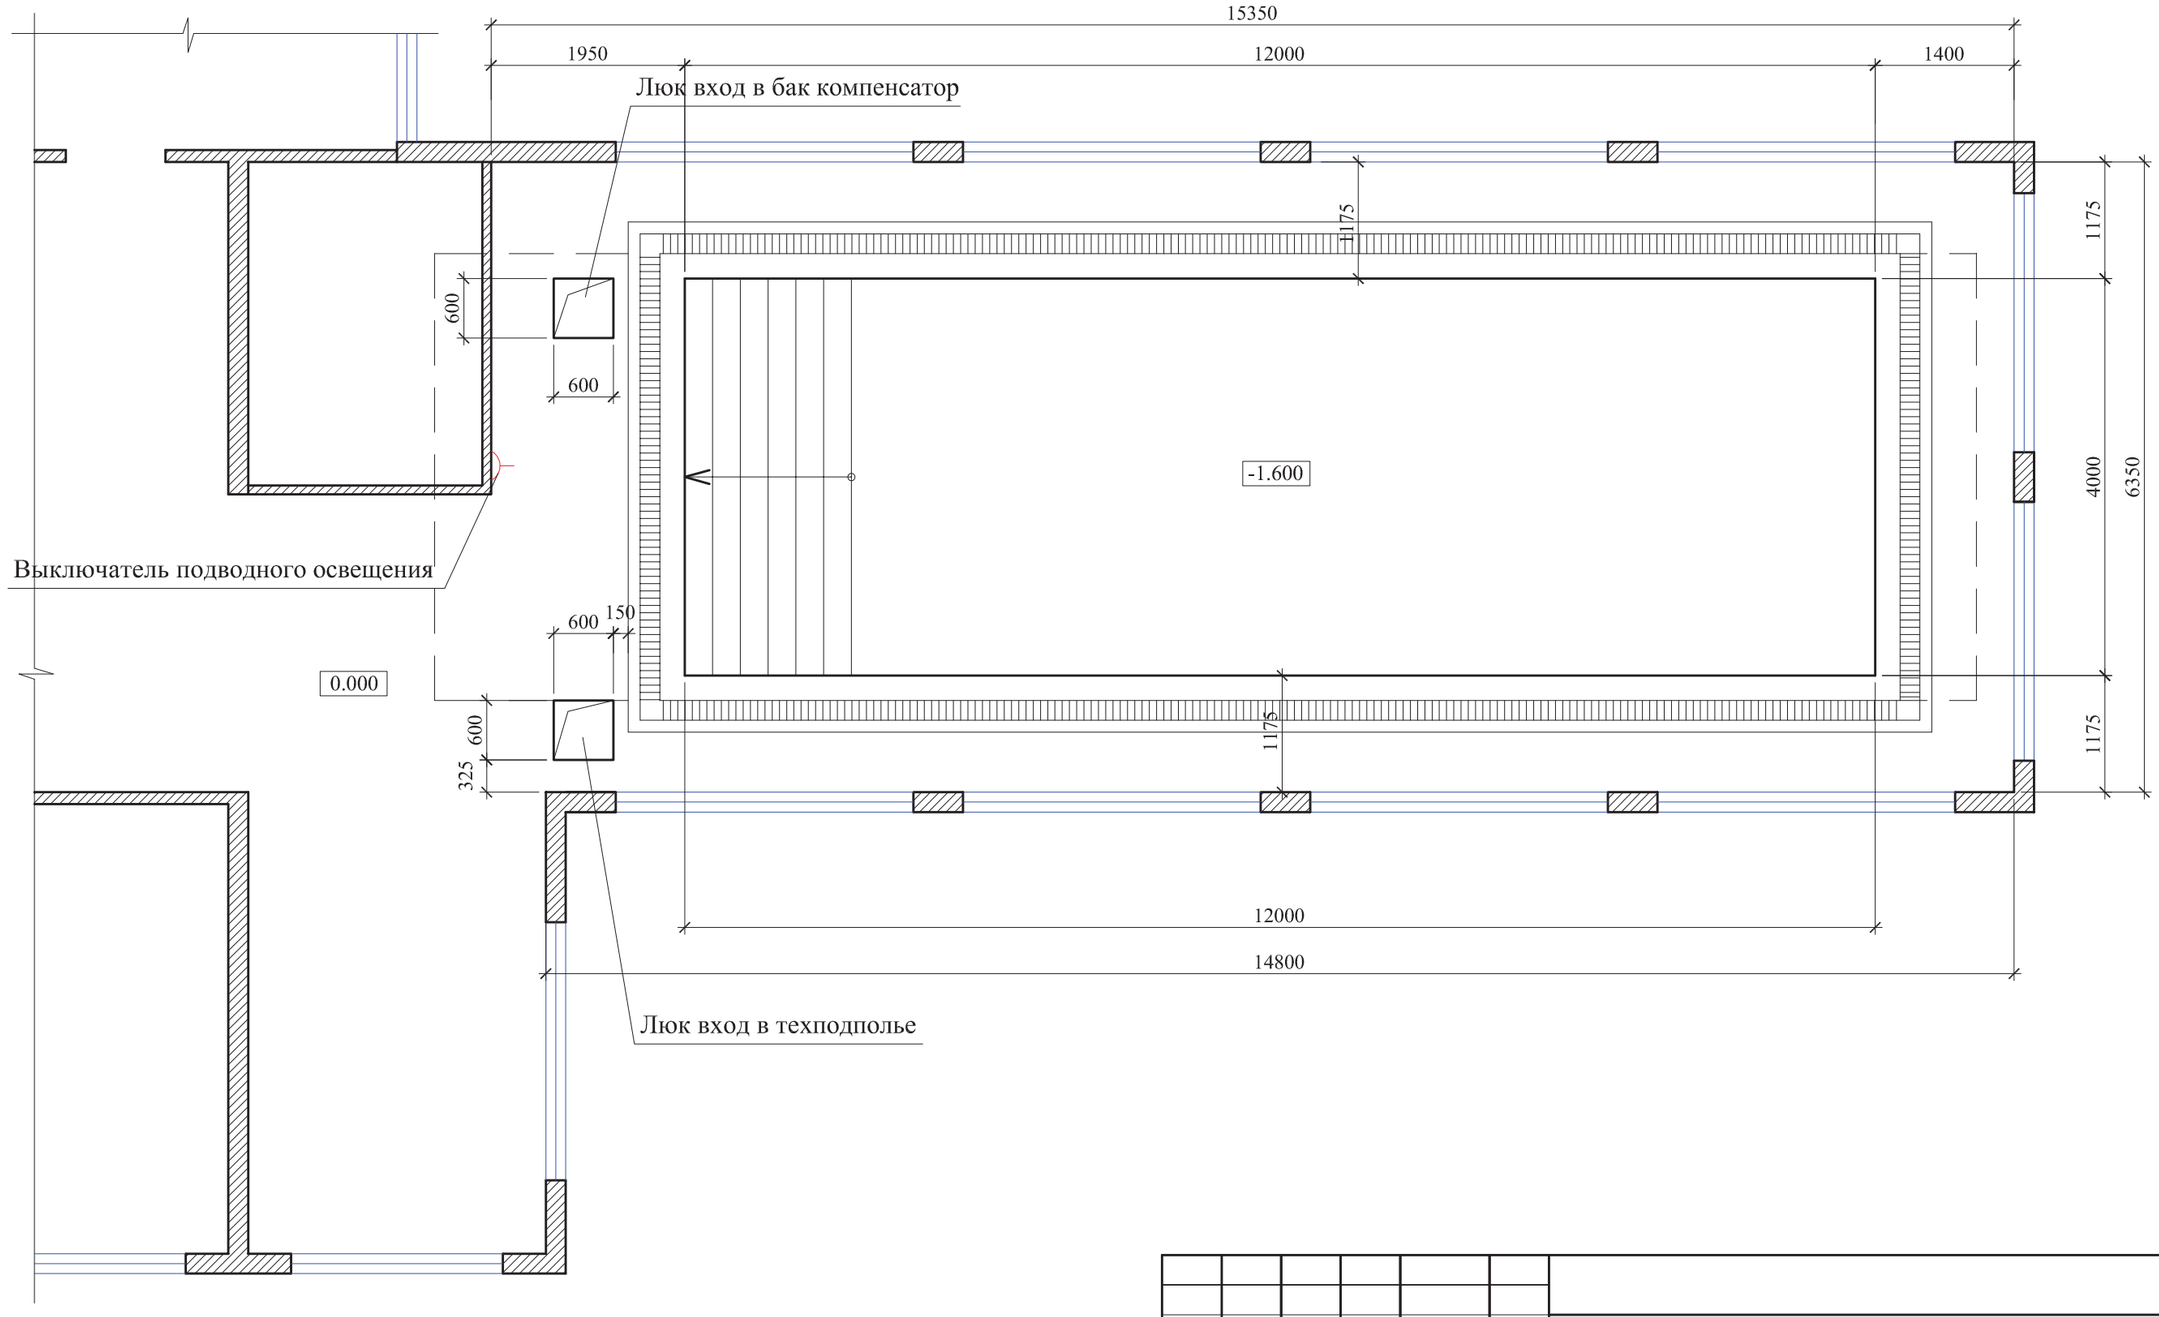

1. За относительную отметку 0,000 принята отметка верха борта чаши бассейна.

Изм.	Кол. уч.	Лист	№ док.	Подп.	Дата
ГАП					
ГИП					
Разраб.		Хрхрян			04.2019
Проверил					

Проект плавательного бассейна в индивидуальном жилом доме.

Плавательный бассейн.	Стадия	Лист	Листов
	Р	4	20

План расположения бассейна.

ipool бассейны & спа

Взам.инв.N

Подпись и дата

Инв.Nподл.

Формат