


			Согласовано			
Инв.№ подл.	Подп. и дата	Взам. инв.№				

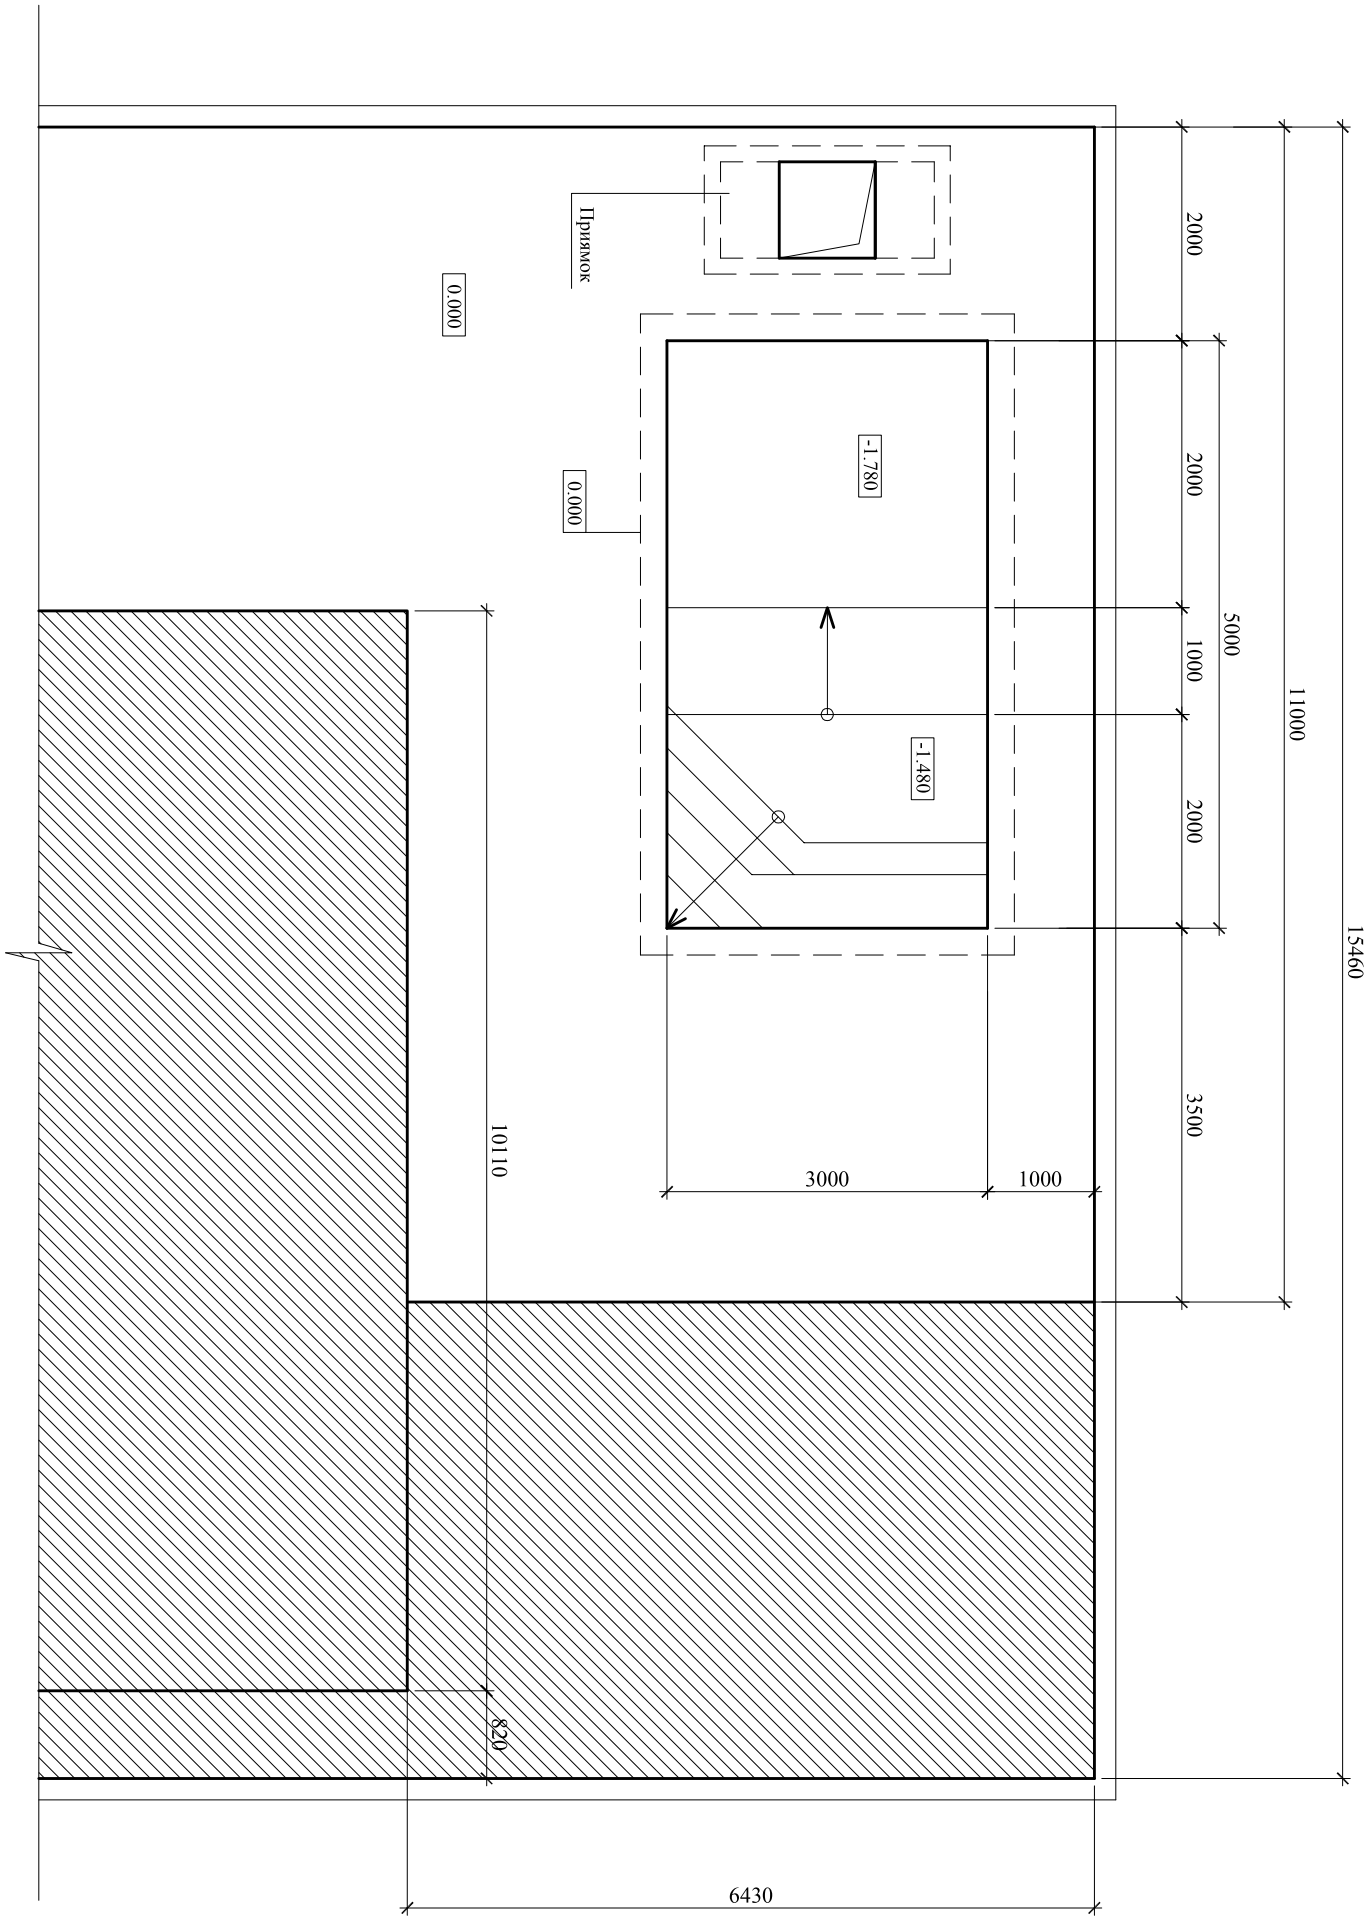

ОМБ - 16 - 006 КЖ									
Скиммерный плавательный бассейн в частном домовладении.									
Изм.	Кол.уч.	Лист	№ док.	Подп.	Дата	Плавательный бассейн			
Разработал									
Проверил									
						План расположения бассейна			
						Стация	Лист	Листов	
						Р	6		

