


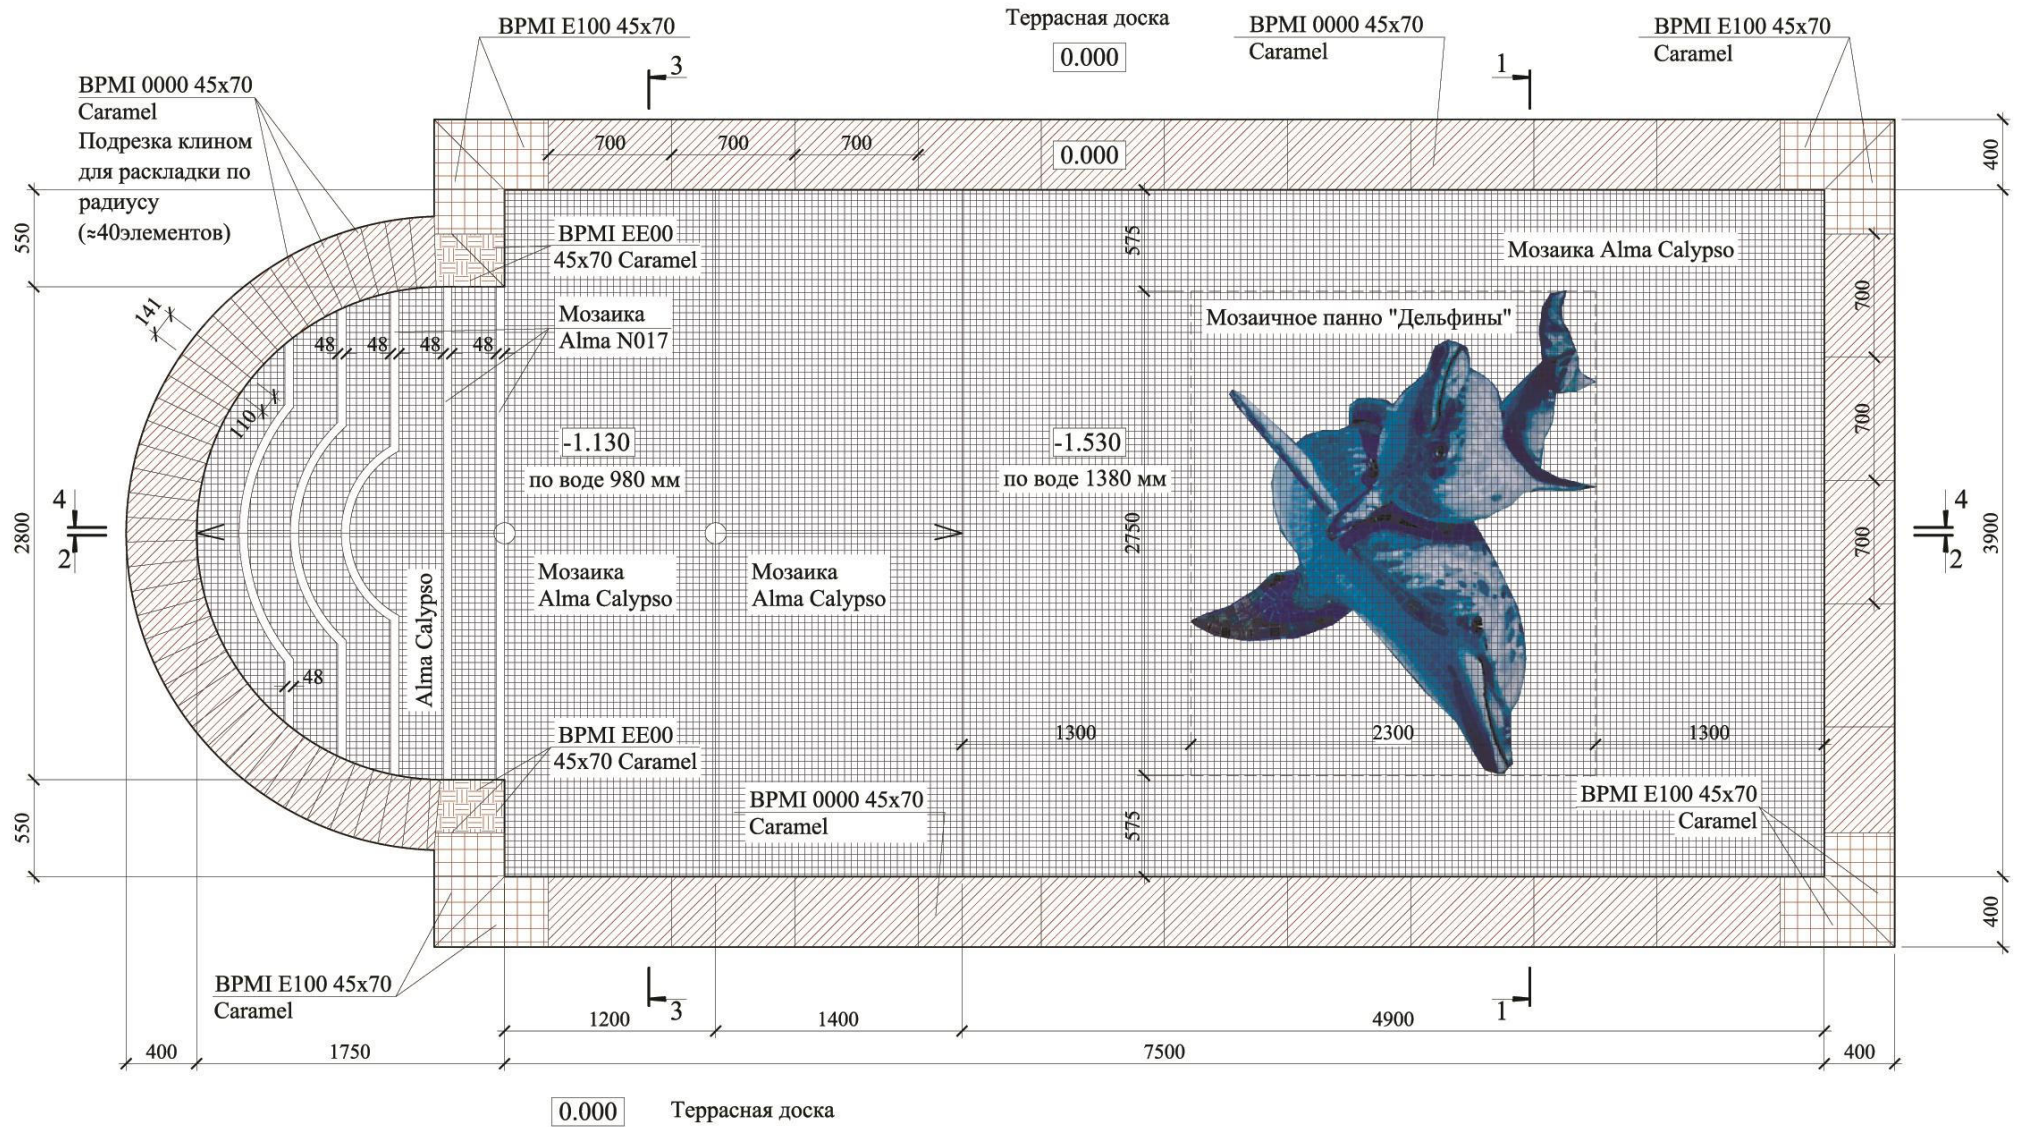

						Открытый плавательный бассейн в г. Ростове-на-Дону по ул. Думчева 6			
Изм.	Колуч.	Лист	Ндок.	Подп.	Дата	Бассейн	Стадия	Лист	Листов
Разработал	Пряникова						Д	1	8
Проверил						План бассейна М 1:30			
									